


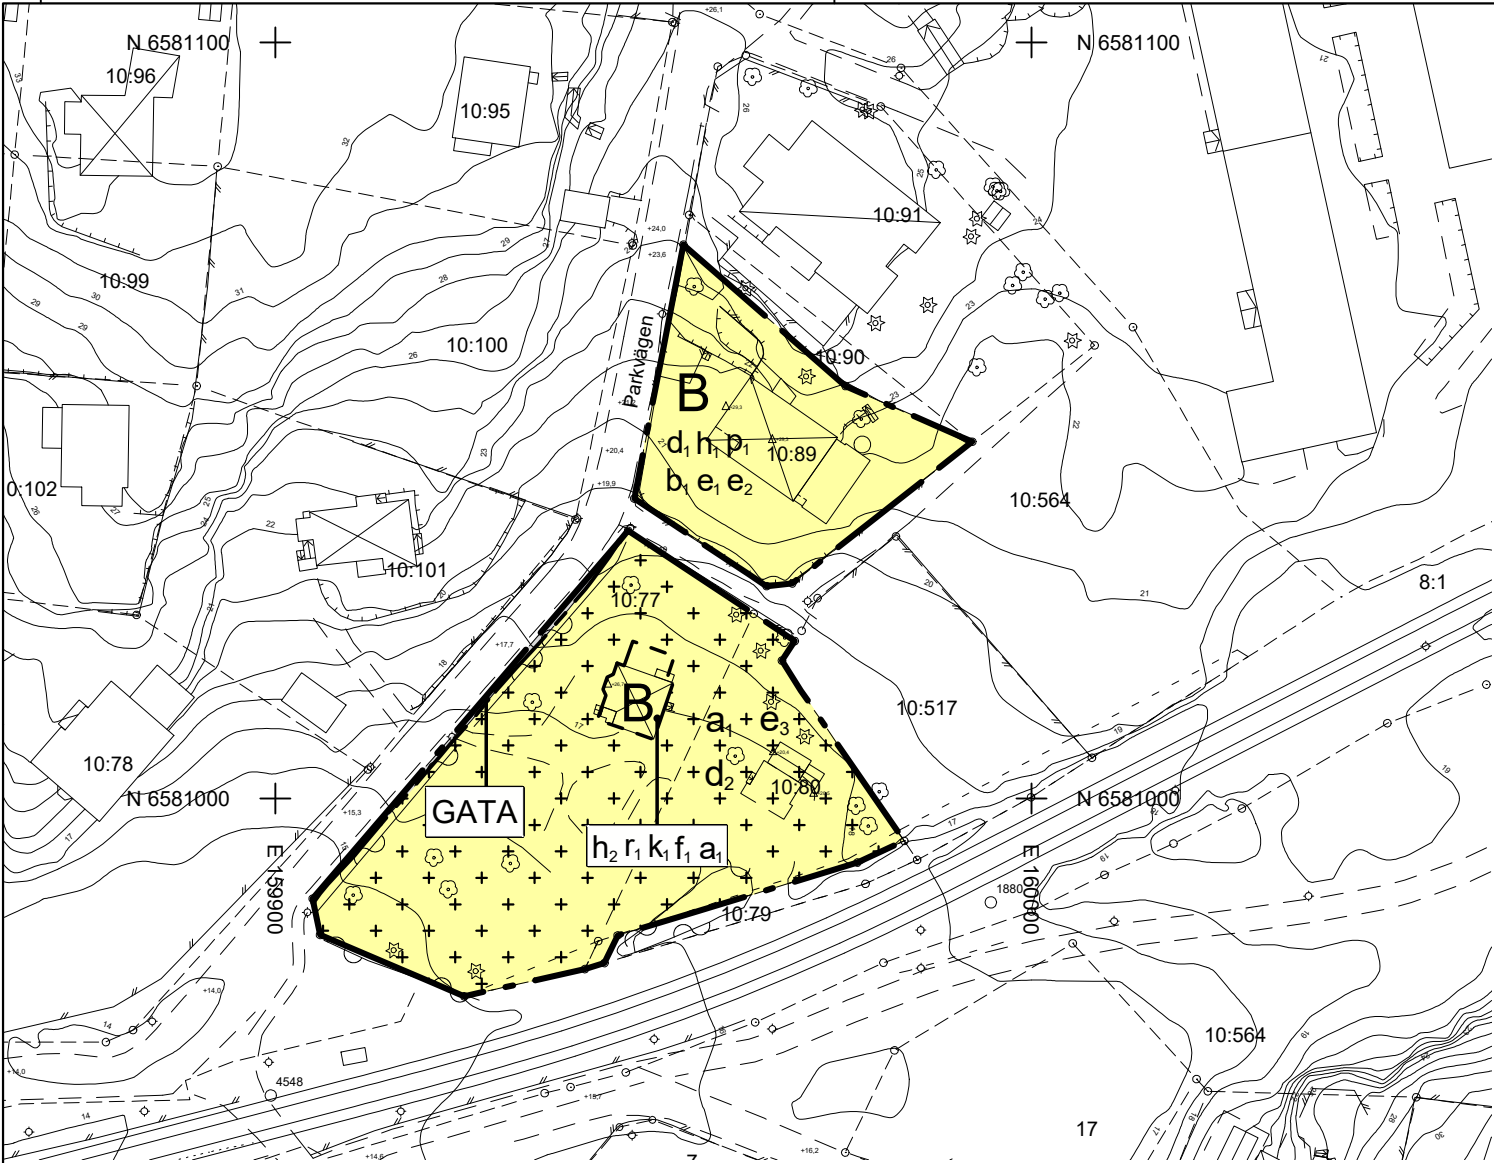

PLANBESTÄMMELSER

Följande gäller inom områden med nedanstående beteckningar. Endast angiven användning och utformning är tillåten.

GRÄNSBETECKNINGAR

- Planområdesgräns
- Användningsgräns
- Egenskapsgräns

ANVÄNDNING AV MARK OCH VATTEN

Allmän plats

GATA Gata.

Kvartersmark

B Bostäder.

EGENSKAPSBESTÄMMELSER FÖR KVARTERSMARK

Begränsning av markens utnyttjande

Marken får endast förses med komplementbyggnader och andra anläggningar än byggnader

Fastighetsstorlek

- d₁ Minsta fastighetsstorlek är 1000 m²
- d₂ Minsta fastighetsstorlek är 2300 m²

Höjd på byggnadsverk

- Högsta nockhöjd för komplementbyggnader är 4 meter
- Högsta byggnadshöjd för komplementbyggnader är 3 meter
- h₁ Högsta nockhöjd är 31 meter över angivet nollplan
- h₂ Högsta nockhöjd är 27 meter över angivet nollplan

Placering

- Komplementbyggnad ska placeras minst 3 meter från fasthetsgräns
- p₁ Huvudbyggnad ska placeras minst 3,5 meter från fasthetsgräns

Rivningsförbud

- r₁ Byggnad får inte rivas

Utformning

- Huvudbyggnad ska uppföras friliggande. Endast en bostad får inredas i byggnaden
- Byggnader ska utformas med sadeltak, mansardtak eller valmat tak.
- f₁ Tillbyggnad på ursprunglig byggnadsvolym ska göras varsamt och ta hänsyn till befintlig karaktär så att tillbyggnaden uppfattas som en väl integrerad del till den ursprungliga gestaltningen.

Utförande

- Minst 60 % av fastighetsarean ska vara genomsläpplig
- Takvatten ska infiltreras inom fastigheten
- b₁ Byggnader ska placeras och utformas efter befintlig terräng. Sprängning, schaktning och fyllning ska minimeras. Mindre nivåskillnader upptas med förhöjd sockel. Schaktning och fyllning är inte tillåtet förutom i direkt anslutning till planerad byggnad eller för att möjliggöra infart till byggnaden.

Utnyttjandegrad

- Endast en huvudbyggnad per fastighet
- e₁ Största byggnadsarea för huvudbyggnad är 200 m²
- e₂ Största sammanlagda byggnadsarea för komplementbyggnader är 40 m². I komplementbyggnad får bostad ej inredas.
- e₃ Största sammanlagda byggnadsarea för komplementbyggnader är 80m², varav den enskilt största byggnaden får vara högst 40m². I komplementbyggnad får bostad ej inredas

Varsamhet


- k₁ Kulturhistoriskt särskilt värdefull byggnad. Ändring av byggnad ska utföras varsamt så att hänsyn tas till byggnadens karaktär som enkel jugendvilla från tidigt 1900-tal vad avser volym, proportioner, utformning och detaljeringsnivå.

Ändrad lovplikt

- Marklov krävs även för markåtgärder som kan försämma markens genomsläpplighet.
- a₁ Byggllov krävs även för komplementbyggnad, komplementbostadshus, tillbyggnader, takkupor samt inredning av ytterligare bostad som annars är lovbeprättad enligt PBL 9 kap. 4 a-c §§..

Genomförandetid


Genomförandetiden är 5 år från det datum detaljplanen får laga kraft

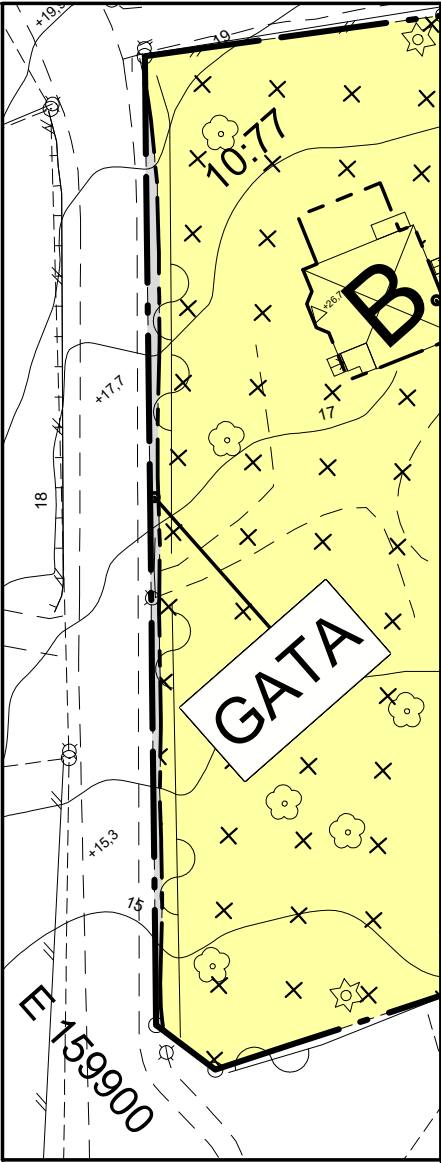

Plankarta. Skala 1:1000

GRUNDKARTA
Ajoudförd endast i planområdet
Mättnoggrannhet: HMK bil. F
Koordnatsystem i plan: SWEREF 99 18 00
i höjd: RH 2000
K-E Vikdahl
Mättningsingenjör

- Beteckningar till grundkartan
- Användningsgräns sammanfallande med fasthetsgräns
 - Användningsgräns ej sammanfallande med fasthetsgräns
 - Fasthetsgräns med gränspunkter
 - Egenskapsgräns
 - Gräns mellan PARK och GATA
 - 5 8:77 Fasthetsbeteckning
 - Staket respektive häck
 - Mur respektive stödmur
 - Väggkant
 - Stig
 - Fastlagd gatuhöjd respektive mått gatuhöjd
 - Bostadshus, gårdsbyggnad respektive annan byggnad
 - Terrestert inmätt
 - Fotogrammetiskt inmätt byggnad
 - Nivåkurva
 - Inmätta lövträd respektive barrträd
 - Lövskog respektive barrskog
 - Trappa, pilen pekar uppåt
 - Tunnel
 - Lr Ledningsrätt
 - ga Gemensamhetsanläggning
 - s Servitut
 - S Samfällt område

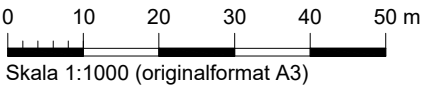

Skala 1:1000 (originalformat A3)

Tillhör Lidingö miljö- och stadsbyggnadsnämnds beslut den 21 november 2023, § 184

Camilla Vikman
Sekreterare

Del av plankarta. Skala 1:500

UPPLYSNINGAR

Planen upprättas enligt plan- och bygglagen (2010:900) i sin lydelse från 1 januari 2015 och handläggs med standardförfarande.

Till planen hör förutom denna plankarta med bestämmelser en planbeskrivning i vilken genomförandefrågor ingår.

Planavgift ska tas ut i samband med bygglov.

LIDINGÖ STAD		Beslut	
Detaljplan för		Uppdrag	KS 2022-03-23, § 3
Parkvägen 8 och Parkvägen 14		Samråd	MSN 2022-12-13, § 245
Lidingö 10:77, Lidingö 10:80 och Lidingö 10:89, stadsdelen Skårsåtra		Granskning	MSN 2023-04-25, § 68
Miljö- och stadsbyggnadskontoret 2023-06-08		Antagande	MSN 2023-11-21, § 184
		ANTAGANDE	
		LAGA KRAFT 2023-12-19	
Per Dunberg		Ida Aronsson	Alexander Celebioglu
Planchef		Planarkitekt	Arkitekt, Sweco
Dnr	Genomförandetid	Arkivbeteckning	
MSN/2021:223	2023-12-19 -- 2028-12-19		